PLAN (kapak açık konumda)

Ölçek 1:50

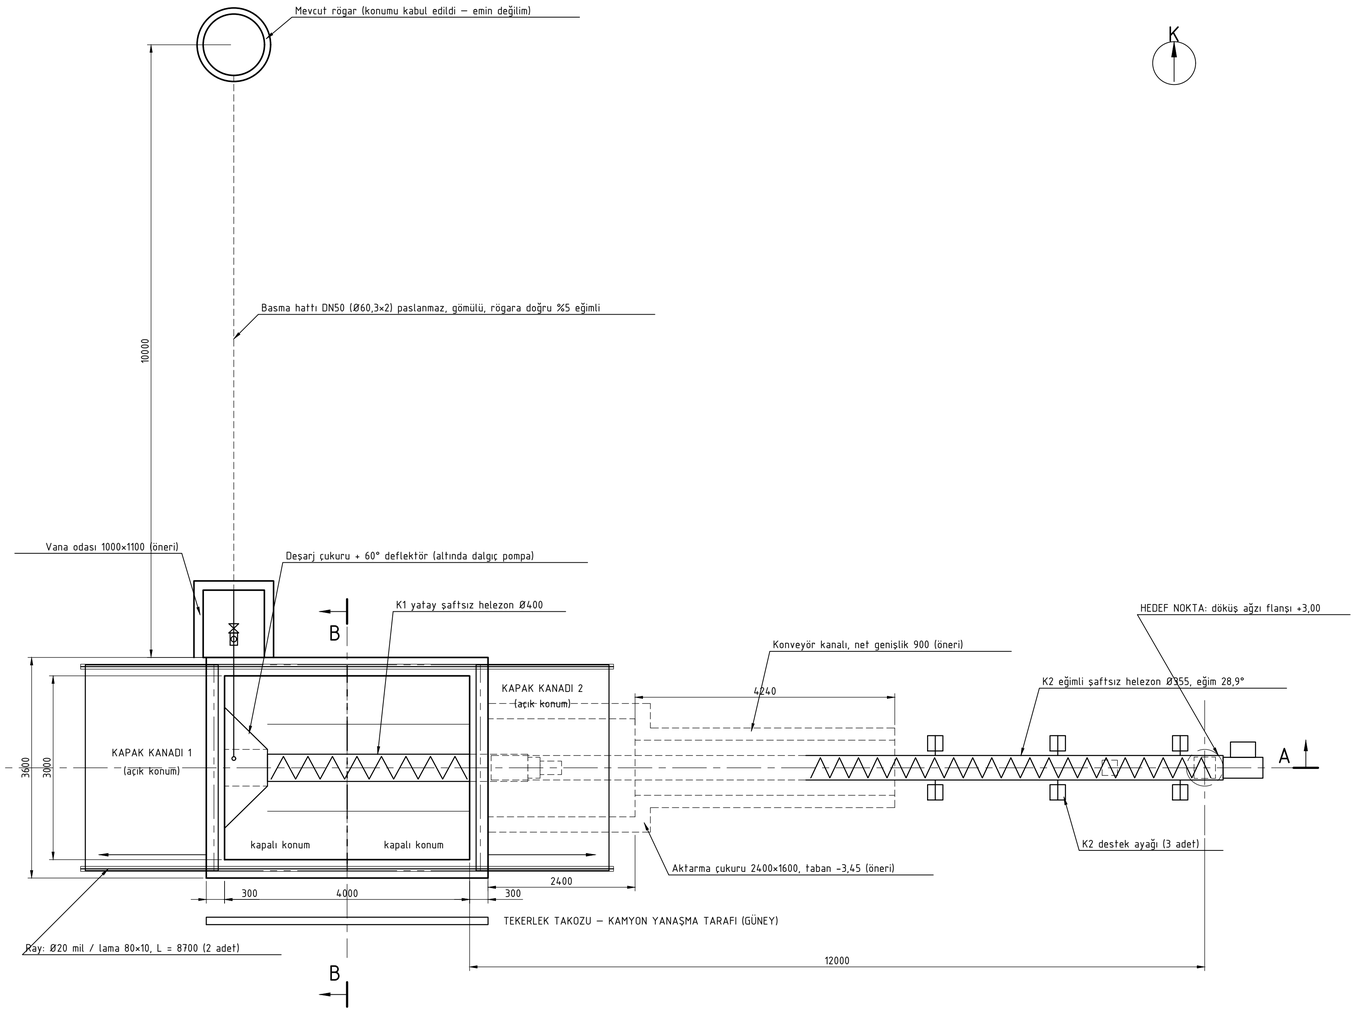

GENEL NOTLAR

1. Ölçüler mm, kotlar m. ±0,00 = zemin = bunker duvar üstü. Koordinat başlangıcı: X = 0 çıkış duvarı iç yüzü, Y = 0 oluk ekseni. Kuzey planın üstüdür (kullanıcı onayı).
2. Kullanıcının taban çizimi (0 katmanı) değiştirilmedi. Bu paftadaki bunker, tarife göre SİMETRİK çizildi (1200 / 600 / 1200); taban çiziminin planında oluk 277 mm kaçık.
3. Siyah/beyaz kalın çizgi: mevcut beton. Turuncu (CL-BETON-EK): ÖNERİLEN ek inşaat işleri — çıkış duvarında K1 geçiş boşluğu 560×560, aktarma çukuru, konveyör kanalı, deşarj çukuru, vana odası, ray temelleri, destek ayağı temelleri, oluk içi eğim betonu. Statik hesap ve donatı kapsam dışıdır.
4. Konveyör: K1 yatay şaftsız helezon Ø400 (çıkarıcı) + K2 eğimli şaftsız helezon Ø355. K2 EĞİMİ 28,9° — İSTENEN 25° SINIRI AŞILIYOR (kullanıcı onayıyla; hedef 12 000 mm noktasında tutuldu). Şaftsız U-oluk helezonlar için üretici sınırı 30°.
5. Şart: 20 m^3 / 4 h = 5,0 m^3/h. Tasarım debisi 6,0 m^3/h (3,3 h). Seçim ve kapasite hesabı: Pafta 02.
6. Geometrik net hacim 19,8 m^3 (3B modelden doğrulandı). Kullanılabilir hacim ≈ 18,8 m^3 (K1 kenarındaki 45° eğim betonu −0,54 m^3; deflektör altı −0,45 m^3).
7. Deşarj çukuru 600×700×700, dalgıç pompa, DN50 PN16 paslanmaz (1.4301) flanşlı basma hattı, çekvalf + sürgülü vana zemin kotundaki vana odasında: Pafta 03.
8. Kapak: 2 kanat, elle, ray üzerinde sürgülü, açıkken bunker ağzı tamamen boş. Yürünebilir: 2,0 kN/m^2 ve 1,5 kN / 200×200 (EN ISO 14122-2). Kar 0,75 kN/m^2 (TS 498, İstanbul II. bölge). Pafta 04–05.
9. Kapak açıkken 2,5 m düşme tehlikesi vardır: döküm yapılmayan kenarlara seyyar korkuluk (h ≥ 1100 mm, EN ISO 14122-3), kamyon tarafına tekerlek takozu konmalıdır.
10. EMİN DEĞİLİM: (a) rögarın konumu — kuzey diş yüzden 10 000 mm, boru ekseninde kabul edildi; (b) K1/K2 motor güçleri ve K1 devri — üretici doğrulamalı; (c) helezon oluk ölçüleri üretici kataloğuna göre değişir; (d) patlayıcı ortam (H2S / CH4) bölge sınıflandırması yapılmadı; (e) K2 destek ayakları ve tüm temeller statik hesaba tabidir.

SİSTEM ÖZETİ		
Büyüklük	Değer	Kaynak / not
Ürün	Susuzlaştırılmış arıtma çamuru, %20–25 KM, yapışkan	kullanıcı
Yığın yoğunluğu	1,05 t/m^3 (aralık 0,88–1,12)	KWS proje verileri
Boşaltma şartı	20 m^3 en çok 4 h; Q ≥ 5,0 m^3/h	kullanıcı
Tasarım debisi	6,0 m^3/h = 6,3 t/h	+%20 pay
K1 (yatay, çıkarıcı)	Şaftsız Ø400, oluk iç 432, L = 4,25 m, 1–6 rpm	Martin tablosu; 2,2 kW (emin değilim)
K2 (eğimli)	Şaftsız Ø355, oluk iç 381, L = 13,54 m, 28,9°, 10–25 rpm	Martin, WAM, OR-TEC; 4,0 kW (emin değilim)
Dalgıç pompa	Grundfos Unilift AP35B.50.08.A1V, 35 mm geçiş, R 2"	üretici veri sayfası
Basma hattı	DN50 PN16, Ø60,3×2,0 — 1.4301; v ≈ 1,2–1,8 m/s	EN 1092-1, EN ISO 1127
Kapak	2 kanat 2170×3360, kanat ≈ 490 kg, hareket 2100 mm	Pafta 04–05

UYGULANAN STANDARTLAR	
Standart	Konu
EN 1092-1	Çelik flanşlar (PN16; DN50–150 için PN10 = PN16)
EN 10365	Sıcak haddelenmiş U, I ve H profiller — ölçü ve kütleler
EN 10219-1/-2	Soğuk şekillendirilmiş kaynaklı kutu profiller
EN 10056-1 / EN 10058	Köşebent / lama (EN 10365 kapsamında değildir) — EKLENDİ
EN 10363	Baklavalı (desenli) saç; DIN 59220 yerine — EKLENDİ
EN 10025-2	S235JR yapı çeliği — EKLENDİ
EN ISO 1461	Sıcak daldırma galvaniz — EKLENDİ
EN 1090-2	Çelik yapıların imalatı (EXC2) — EKLENDİ
ISO 2553	Kaynak sembolleri (Sistem A)
ISO 5817 / ISO 13920	Kaynak kalitesi C / kaynaklı imalat toleransı — EKLENDİ
ISO 128, ISO 129-1	Teknik resim genel kuralları ve ölçülendirme
ISO 3098, 5455, 5457, 7200	Yazı, ölçek, pafta boyutu, antet — EKLENDİ
EN ISO 13857	Güvenlik mesafeleri
EN 618	Dökme malzeme taşıma donanımı güvenliği — EKLENDİ
EN ISO 14122-2 / -3	Yürüme platformu yükleri / korkuluk — EKLENDİ
EN 558; EN 1074-1/-2; EN 1171	Vana yüzden yüze boyları; sürgülü vana — EKLENDİ
EN 12050-4	Atık su çekvalfleri — EKLENDİ
EN 1514-1 / EN 1515-1	Flanş contaları / cıvataları — EKLENDİ
EN ISO 1127 / EN 10217-7	Paslanmaz kaynaklı boru ölçüleri — EKLENDİ
EN 12056-4	Basma hattı akış hızı 0,7–2,3 m/s — EKLENDİ
TS 498	Kar yükü — EKLENDİ

A-A KESİTİ (boyuna, eksende)

Ölçek 1:50

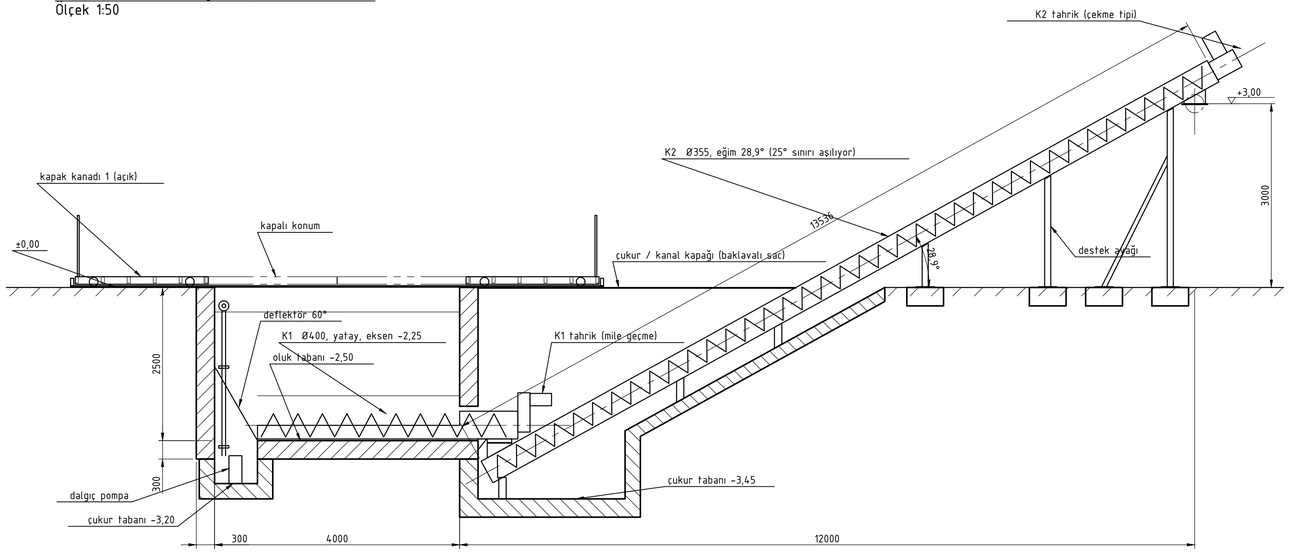

B-B KESİTİ (enine, batıya bakış)

Ölçek 1:50

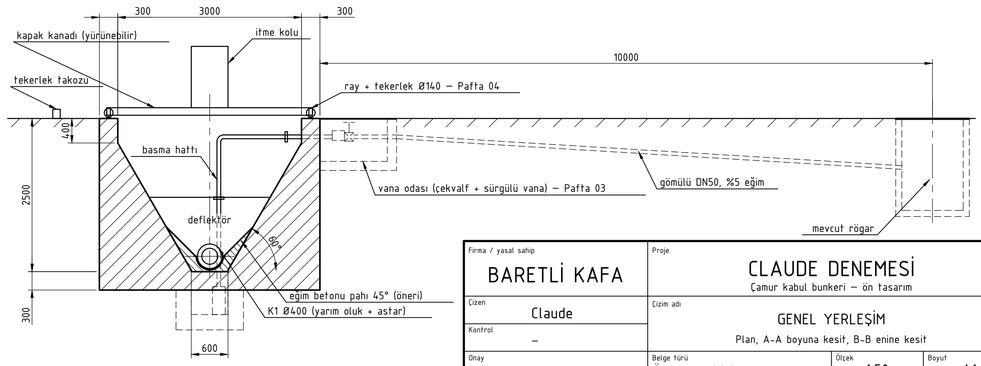

Firma / yasal sahip: BARETLİ KAFA	Proje: CLAUDE DENEMESİ — Çamur kabul bunkeri — ön tasarım		
Çizen: Claude	Çizim adı: GENEL YERLEŞİM — Plan, A-A boyuna kesit, B-B enine kesit		
Kontrol: —			
Onay: —	Belge türü: Ön tasarım çizimi	Ölçek: 1:50	Boyut: A1
Tarih: 2026-10-07	Çizim no: CD-BNK-01	Rev.: A	Pafta: 1 / 6