KESİT E-E — deşarj çukuru

Ölçek 1:10 (boyuna, kuzeye bakış)

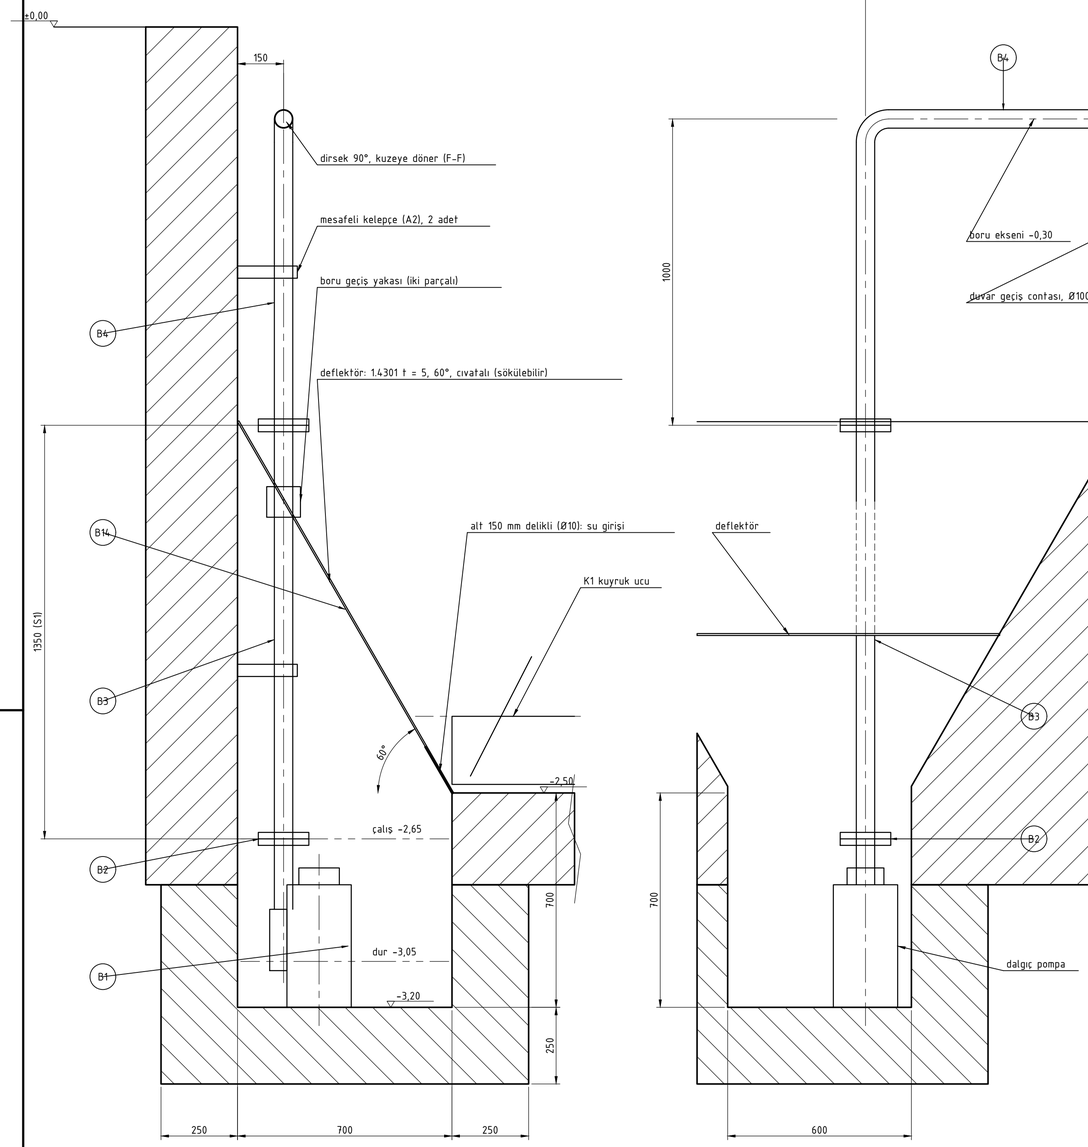

KESİT F-F — basma hattı ve vana odası

Ölçek 1:10 (enine, batıya bakış; kuzey sağda)

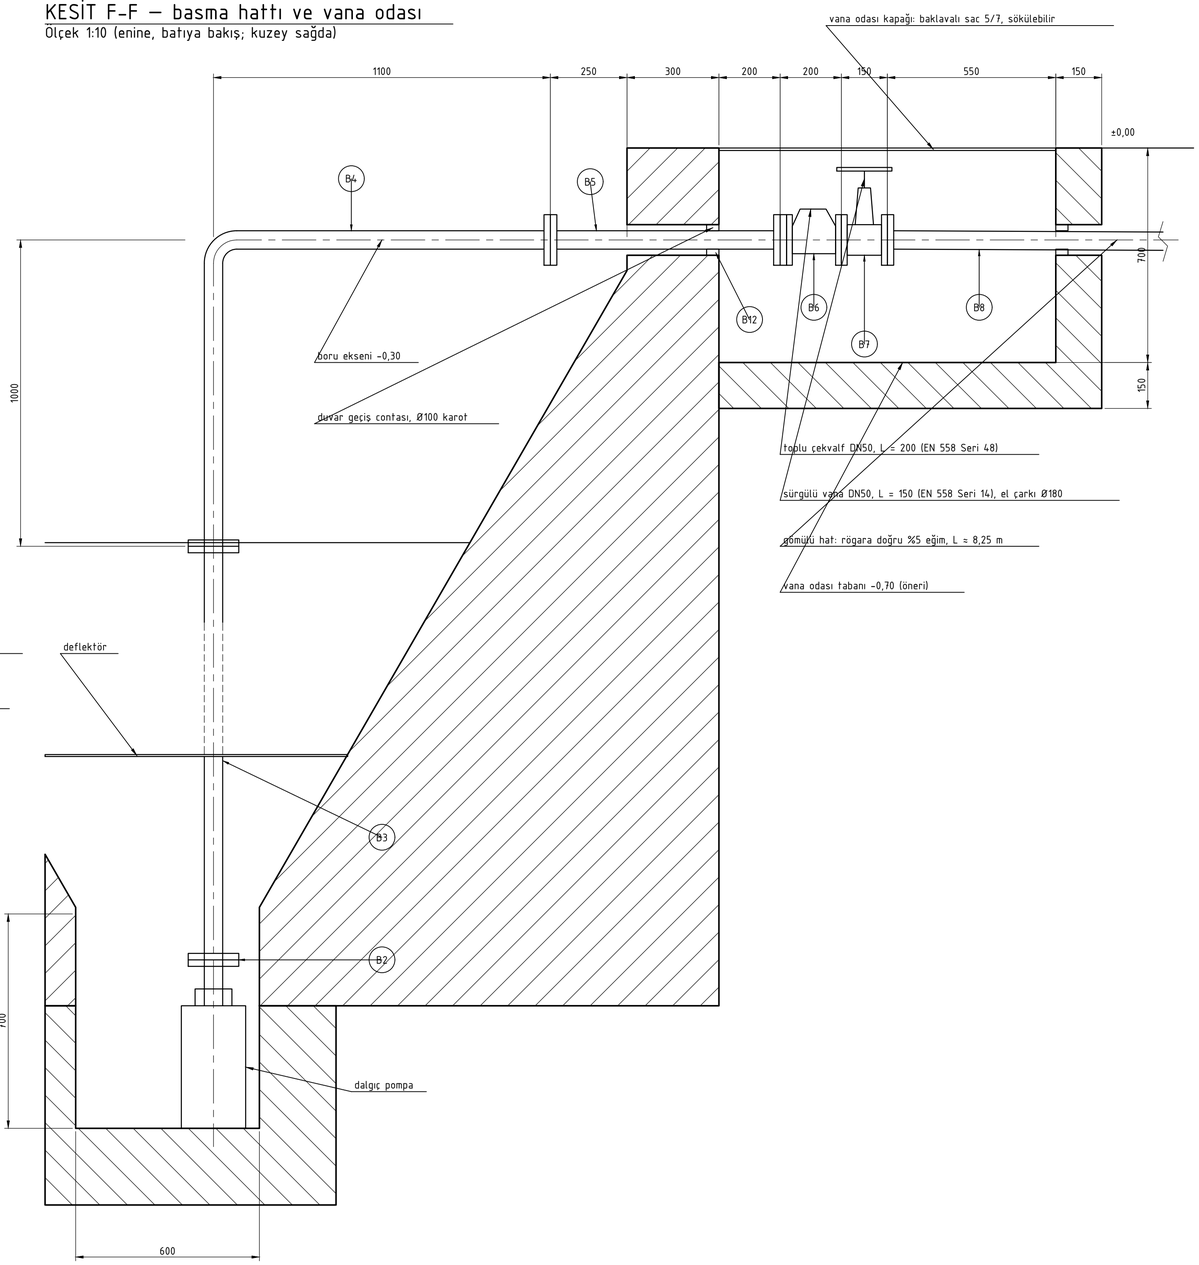

VANA ODASI — PLAN (kapak kaldırılmış)

Ölçek 1:10

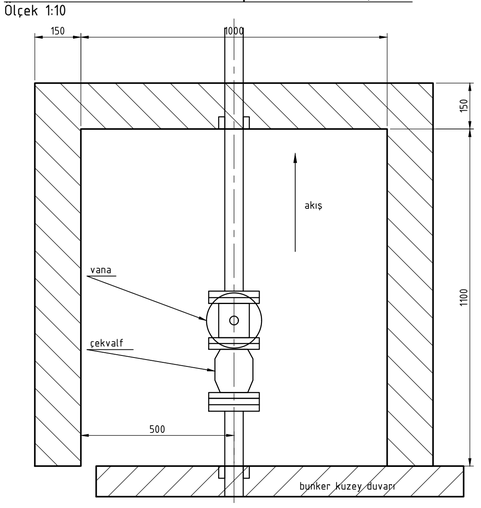

DETAY — flanş bağlantısı DN50 PN16

Ölçek 1:2 (EN 1092-1 Tip 01)

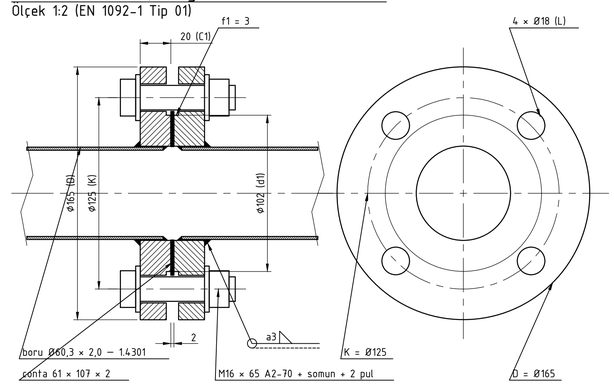

NOTLAR VE HİDROLİK KONTROL

1. Pompa: Grundfos Unilift AP35B.50.08.A1V (şamandıralı, 35 mm serbest geçiş, Rp 2, 1×230 V, P1 = 1,25 kW). Üreticinin en küçük çukur ölçüsü Ø550 × 600 mm; bu çukur 600 × 700 × 700 mm.
2. Şamandıra: çalış 550 mm, dur 150 mm (çukur tabanından; uzun kablo ayarı). Aktif hacim ≈ 155 L. En kötü durumda saatte ≈ 26 kalkış; izin verilen kalkış sayısı üretici kılavuzundan doğrulanmalı (EMİN DEĞİLİM).
3. Hidrolik ön hesap: iç çap 56,3 mm; statik yükseklik 2,4–2,75 m; hat ≈ 13 m; f ≈ 0,023; yerel kayıp katsayıları toplamı ≈ 5 (kabul). İşletme noktası ≈ 4,4 l/s, ≈ 4,5 m; hız ≈ 1,8 m/s — 0,7–2,3 m/s aralığında (EN 12056-4).
4. Tüm bağlantılar flanşlı: EN 1092-1 Tip 01, PN16, 1.4301. DN50–150 için PN10 ve PN16 ölçüleri aynıdır. C1 = 20 mm alındı; bir kaynak 19 mm veriyor: siparişte imalatçı belgesiyle doğrulanmalı.
5. Çekvalf gövdesi PN10, flanş delgisi PN10/16. Hat basıncı 1 bar altında olduğundan uygundur. Yatay monte edilir, kapak üstte. Görevi rögardan geri tepmeyi önlemektir.
6. Pompa durunca vana odasından sonraki hat rögara, yükselen boru çukura boşalır (≈ 6,5 L): hatta su kalmaz.
7. Pompa bakımı: bunker boş ve yıkanmış olmalı; deflektör sökülür, −1,30 kotundaki flanş açılır, pompa S1 makarasıyla birlikte zincirle alınır. Kapalı alan giriş kuralları uygulanır.
8. Çukur, vana odası ve duvar delikleri ÖNERİDİR; statik ve yalıtım detayı inşaat projesinde çözülür.

BASMA HATTI MALZEME LİSTESİ

Poz	Tanım	Ölçü / standart	Adet
B1	Dalgıç pompa, şamandıralı	Grundfos Unilift AP35B.50.08.A1V; Rp 2; 1×230 V	1
B2	Dişli flanş + nipel (pompa çıkışı)	DN50 PN16, EN 1092-1 Tip 13, R 2, 1.4301	1
B3	Boru makarası S1 (düşey)	Ø60,3×2,0; L = 1350; 2 flanş Tip 01	1
B4	Boru makarası S2 (düşey + dirsek + yatay)	924 + dirsek 90° r = 76 + 974; 2 flanş	1
B5	Duvar geçiş makarası S3	Ø60,3×2,0; L = 750; 2 flanş	1
B6	Toplu çekvalf	DN50, AVK 53/35, L = 200, EN 12050-4	1
B7	Sürgülü vana (elastomer sıftl)	DN50 PN10/16, AVK 06/80, L = 150, EN 1074-2	1
B8	Çıkış makarası S4 + gömülü boru	Ø60,3×2,0; L ≈ 8,95 m; 1 flanş; kaynaklı ek	1
B9	Flanş (makaralara dahil)	EN 1092-1 Tip 01, DN50 PN16, 1.4301	7
B10	Conta	EN 1514-1 IBC, 61×107×2, EPDM	6
B11	Cıvata takımı	M16×65 A2-70 (ISO 4017) + somun + 2 pul	24
B12	Duvar geçiş contası	Hauff HSD100 SG 1×18–65; karot Ø100	3
B13	Mesafeli boru kelepçesi	DN50, A2, duvardan 150 mm	3
B14	Deflektör sacı + boru yakası	1.4301 t = 5; yamuk 600/1975 × 1400; alt 150 delikli	1
B15	Vana odası kapağı	Baklavalı sac 5/7, 2 × (575×1050), köşebent çerçeve	1

ÖLÇÜ TABLOSU — DN50 PN16

Parça	Ölçüler (mm)	Kaynak
Boru DN50	Ø60,3 × 2,0; iç Ø56,3; 2,92 kg/m; 1.4301; EN 10217-7 / EN ISO 1127	thyssenkrupp el kitabı
Flanş Tip 01 PN16	D 165; K 125; 4 × Ø18; M16; C1 20; d1 102; f1 3; delik Ø61,5	thyssenkrupp; Roymech C1 = 19
Dirsek 90°	r = 76 (merkezden uca 76); Ø60,3 × 2,0	Kindlimann (EN 10253)
Conta	iç Ø61 × dış Ø107; t = 2 (kalınlık kabul)	Gore tablosu (EN 1514-1)
Cıvata	M16 × 65: 20 + 20 + 2 + 2×3 + 13 + 4 = 65 (hesap)	Wermac: Tip 11 çift M16×60
Sürgülü vana	L 150 (EN 558 Seri 14); H3 319; el çarkı Ø180; 9,6 kg	AVK 06/80-006
Toplu çekvalf	L 200 (EN 558 Seri 48); H 101; 7,5 kg; gövde PN10	AVK 53/35-003
Duvar geçişi	karot Ø100; boru dış çapı 18–65; genişlik 40	Hauff HSD100
Pompa	455 × 234 × 210; 11 kg; Q/H: 1 l/s~10,3 m; 2~8,9; 3~7,4; 4~5,5; 5~3,4	Grundfos veri sayfası

Firma / yasal sahip: BARETLİ KAFA	Proje: CLAUDE DENEMESİ — Çamur kabul bunkeri — ön tasarım		
Çizen: Claude	Çizim adı: DEŞARJ ÇUKURU VE BASMA HATTI — Pompa, DN50 PN16 flanşlı hat, çekvalf, sürgülü vana		
Kontrol: —			
Onay: —	Belge türü: Ön tasarım çizimi	Ölçek: 1:10 / 1:2	Boyut: A1
Tarih: 2026-10-07	Çizim no: CD-BNK-03	Rev.: A	Pafta: 3 / 6