

PLAN — kapak kapalı (açık konum hayali çizgiyle)

Ölçek 1:20

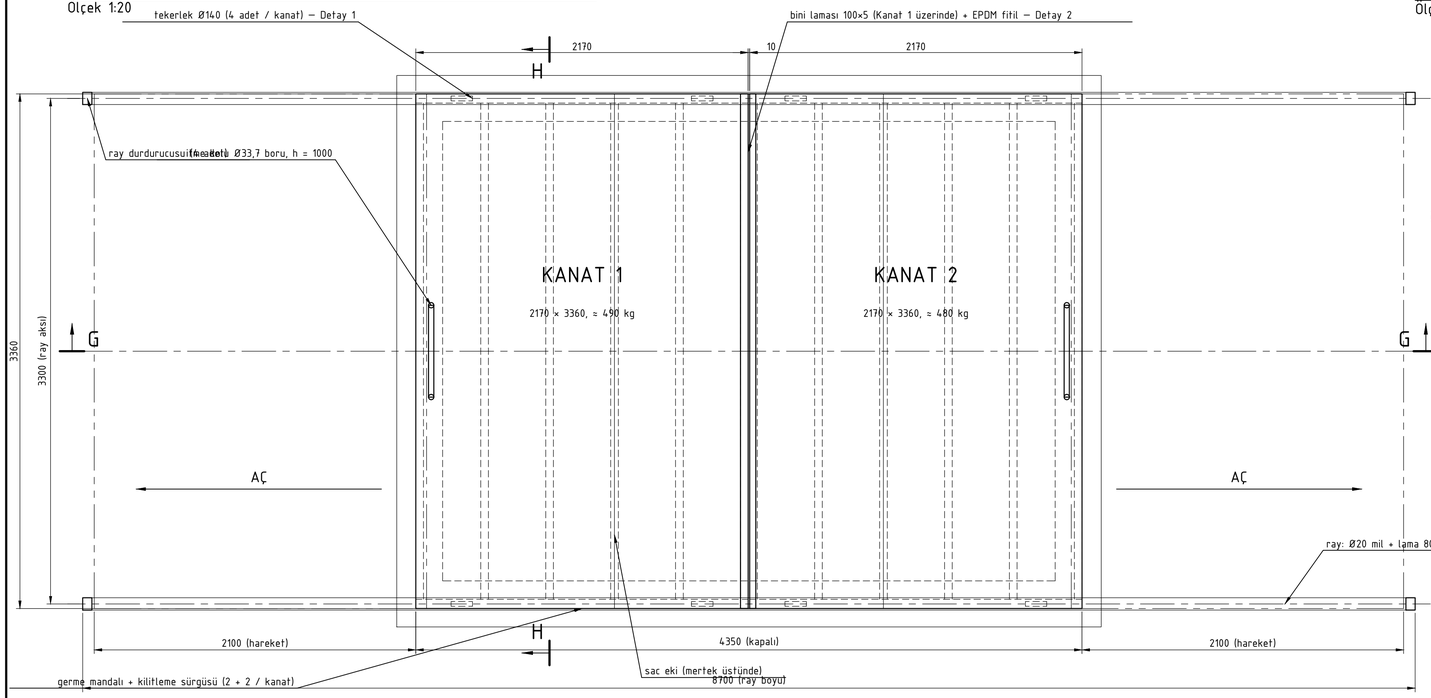

DETAY 1 — ray, tekerlek ve kenar kirişi

Ölçek 1:2

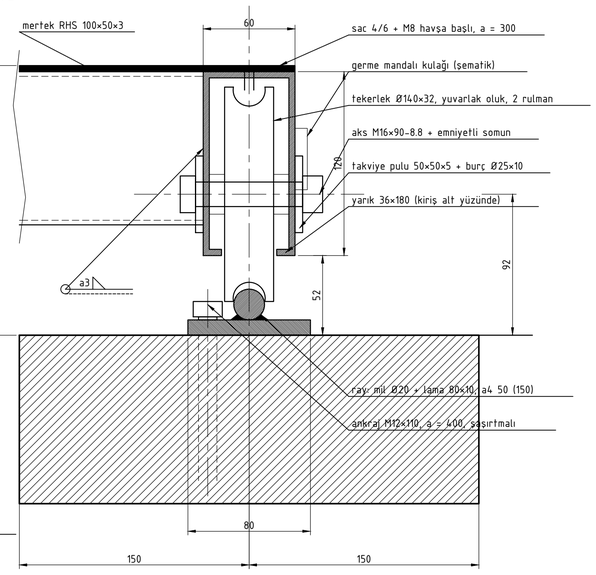


TASARIM NOTLARI

1. Yükler: öz ağırlık ≈ 0,66 kN/m²; yürüme yükü 2,0 kN/m² ve 1,5 kN / 200×200 mm (EN ISO 14122-2); kar 0,75 kN/m² (TS 498, İstanbul, II. bölge). Yürüme yükü belirleyicidir.
2. Mertek RHS 100×50×3 (I = 106 cm⁴, W = 21,3 cm³), açıklık 3,30 m, aralık 424 mm: sehim 7,3 mm = L/450 (sınır L/200); gerilme 99 MPa, sınır 235 MPa (S235).
3. Tekerlek yükü: (490 kg + 2,0 kN/m² × 7,29 m²) / 4 = 494 kg; izin verilen 550 kg (Ø140 tekerlek, çift başına 1100 kg — IBFM).
4. İtme kuvveti: F = c × W / r = 0,5 mm × 4,8 kN / 70 mm ≈ 34 N (yuvarlanma). Kir ve ilk hareket payıyla ≈ 100 N; tek kişi için ilk hareket sınırı 200 N (HSE).
5. Sac 4/6 baklavalı, mertek aralığı 424 mm: nokta yükte sehim ≈ L/300 (yaklaşık hesap — EMİN DEĞİLİM; üretici yük tablosuyla doğrulanmalı).
6. Su: ray altlığı duvar üstüne mastik üzerine oturur ve su eşiği olur; orta ek bini lamasıyla, kısa kenarlar etek lamasıyla kapanır. Zemin duvar üstüyle aynı kotta: yüzey suyu için çevre eğimi inşaat projesinde verilmelidir.
7. Rüzgâr emmesi (0,5 kN/m² × ≈ 1,3) kanat ağırlığına yakındır: kanat kapalı ve açık konumda germe mandalıyla bağlanır (ürün seçimi imalatçıda — EMİN DEĞİLİM).
8. Kullanım: mandallar açılır, kanatlar birbirinden bağımsız itilir, açık konumda yeniden mandallanır. Kapak açıkken düşme tehlikesi vardır: seyyar korkuluk.
9. Malzeme S235JR / S235JRH; sıcak daldırma galvaniz EN ISO 1461 (3–6 mm et kalınlığında ortalama 70 µm). Sac, galvanizden SONRA cıvatayla bağlanır.


DETAY 2 — orta ek, bini laması

Ölçek 1:2

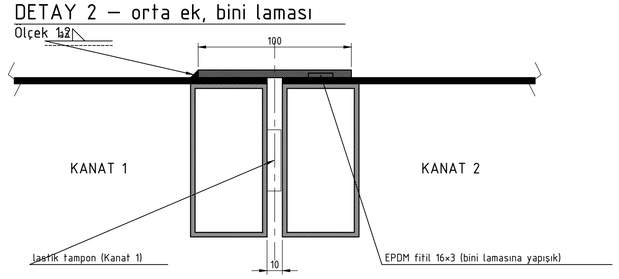

KESİT G–G — boyuna (eksende)


Ölçek 1:20

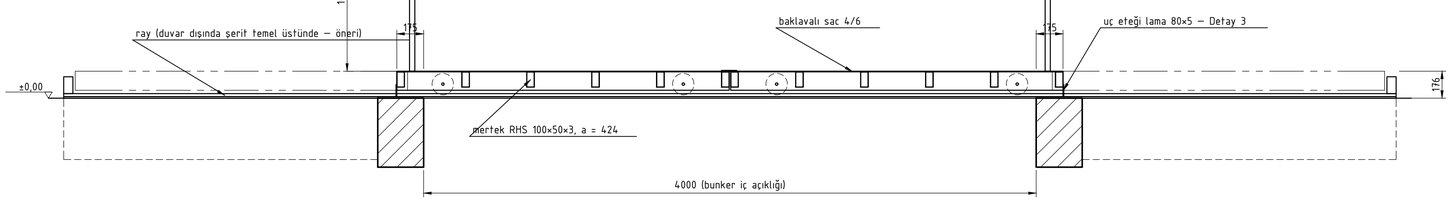

RAY VE SAHA MALZEMESİ					
Poz	Tanım	Ölçü	Adet	kg/m	kg
R1	Ray mili Ø20, S235JR	8700	2	2,47	43,0
R2	Ray altlığı lama 80×10	8700	2	6,28	109,3
R3	Durdurucu plaka 100×60×10 + lastik tampon	—	4	—	1,9
R4	Mandal / sürgü kulağı, lama 60×8	80	16	3,77	4,8
R5	Ankraj M12×110	a = 400	44	—	—
P6	Tekerlek Ø140, yuvarlak oluklu, 2 rulmanlı	IBFM 363	8	—	—
P6a	Aks cıvatası M16×90–8.8 + somun + 2 burç	—	8	—	—
P9	Germe mandalı (A2) / kilitleme sürgüsü Ø16	—	4 / 4	—	—


KESİT H–H — enine (mertek ekseninde)

Ölçek 1:20

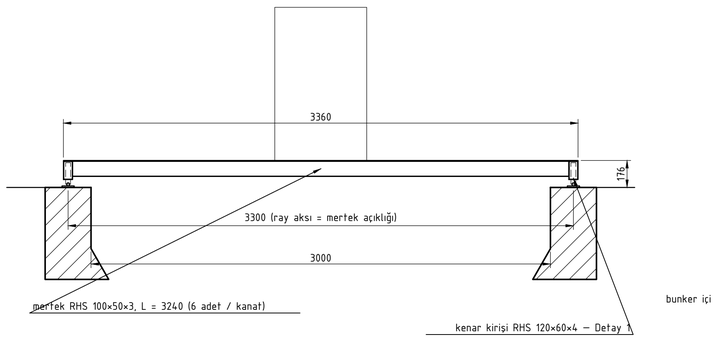

DETAY 3 — uç eteği (kısa kenar)

Ölçek 1:2

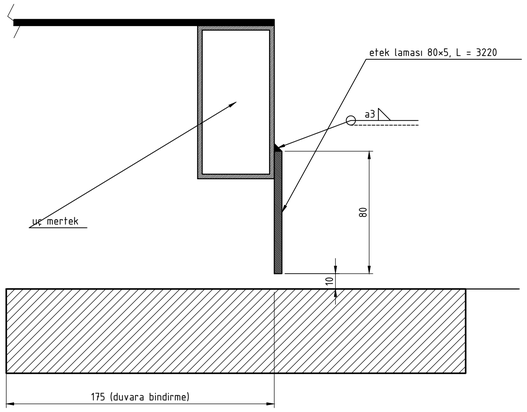

Firma / yasal sahip: BARETLİ KAFA	Proje: CLAUDE DENEMESİ — Çamur kabul bunkeri — ön tasarım		
Çizen: Claude	Çizim adı: SÜRGÜLÜ KAPAK — GENEL — Plan, kesitler, ray ve tekerlek detayları		
Kontrol: —			
Onay: —	Belge türü: Ön tasarım çizimi	Ölçek: 1:20 / 1:2	Boyut: A1
Tarih: 2026-10-07	Çizim no: CD-BNK-04	Rev.: A	Pafta: 4 / 6